



[illegible]



אלומיניום		סוג פח:	-	מתכנן: אור		שם הפרוייקט:		SH_01		מספר פנל:
RAL 9011		צבע	2	תאריך: 12.03.2026		פרופסור שור 9 ת"א		רוחב	אורך	פריסת פח:
		עובי פח:		הזמנה:		מיקום הפנל בבניין:		508	4520	
				SHOR_120326		פלשונגים		4		מספר יחידות:

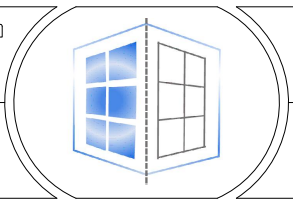



WORK\UR\UR.dwg

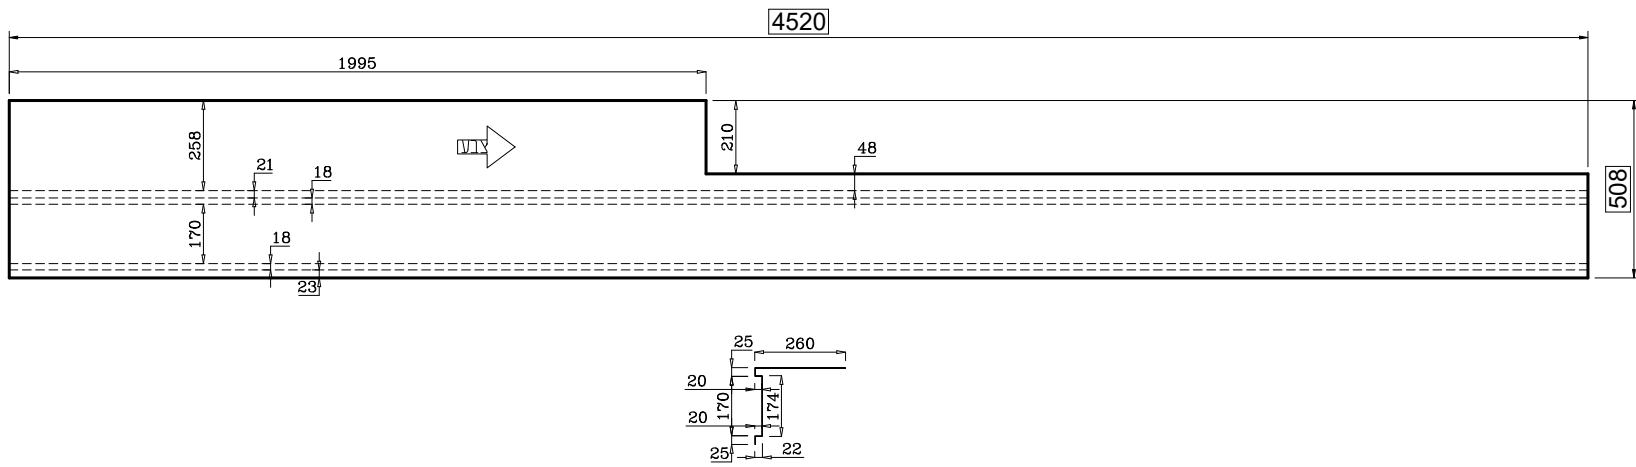



אלומיניום		סוג פח:	-	מתכנן: אור		שם הפרוייקט:		SH_02		מספר פנל:
RAL 9011		עובי פח:	2	תאריך: 12.03.2026		פרופסור שור 9 ת"א		רוחב		פריסת פח:
צבע				הזמנה:		מיקום הפנל בבנין:		1332		אורך
				SHOR_120326		פלשונגים		977		מספר יחידות:
								2		

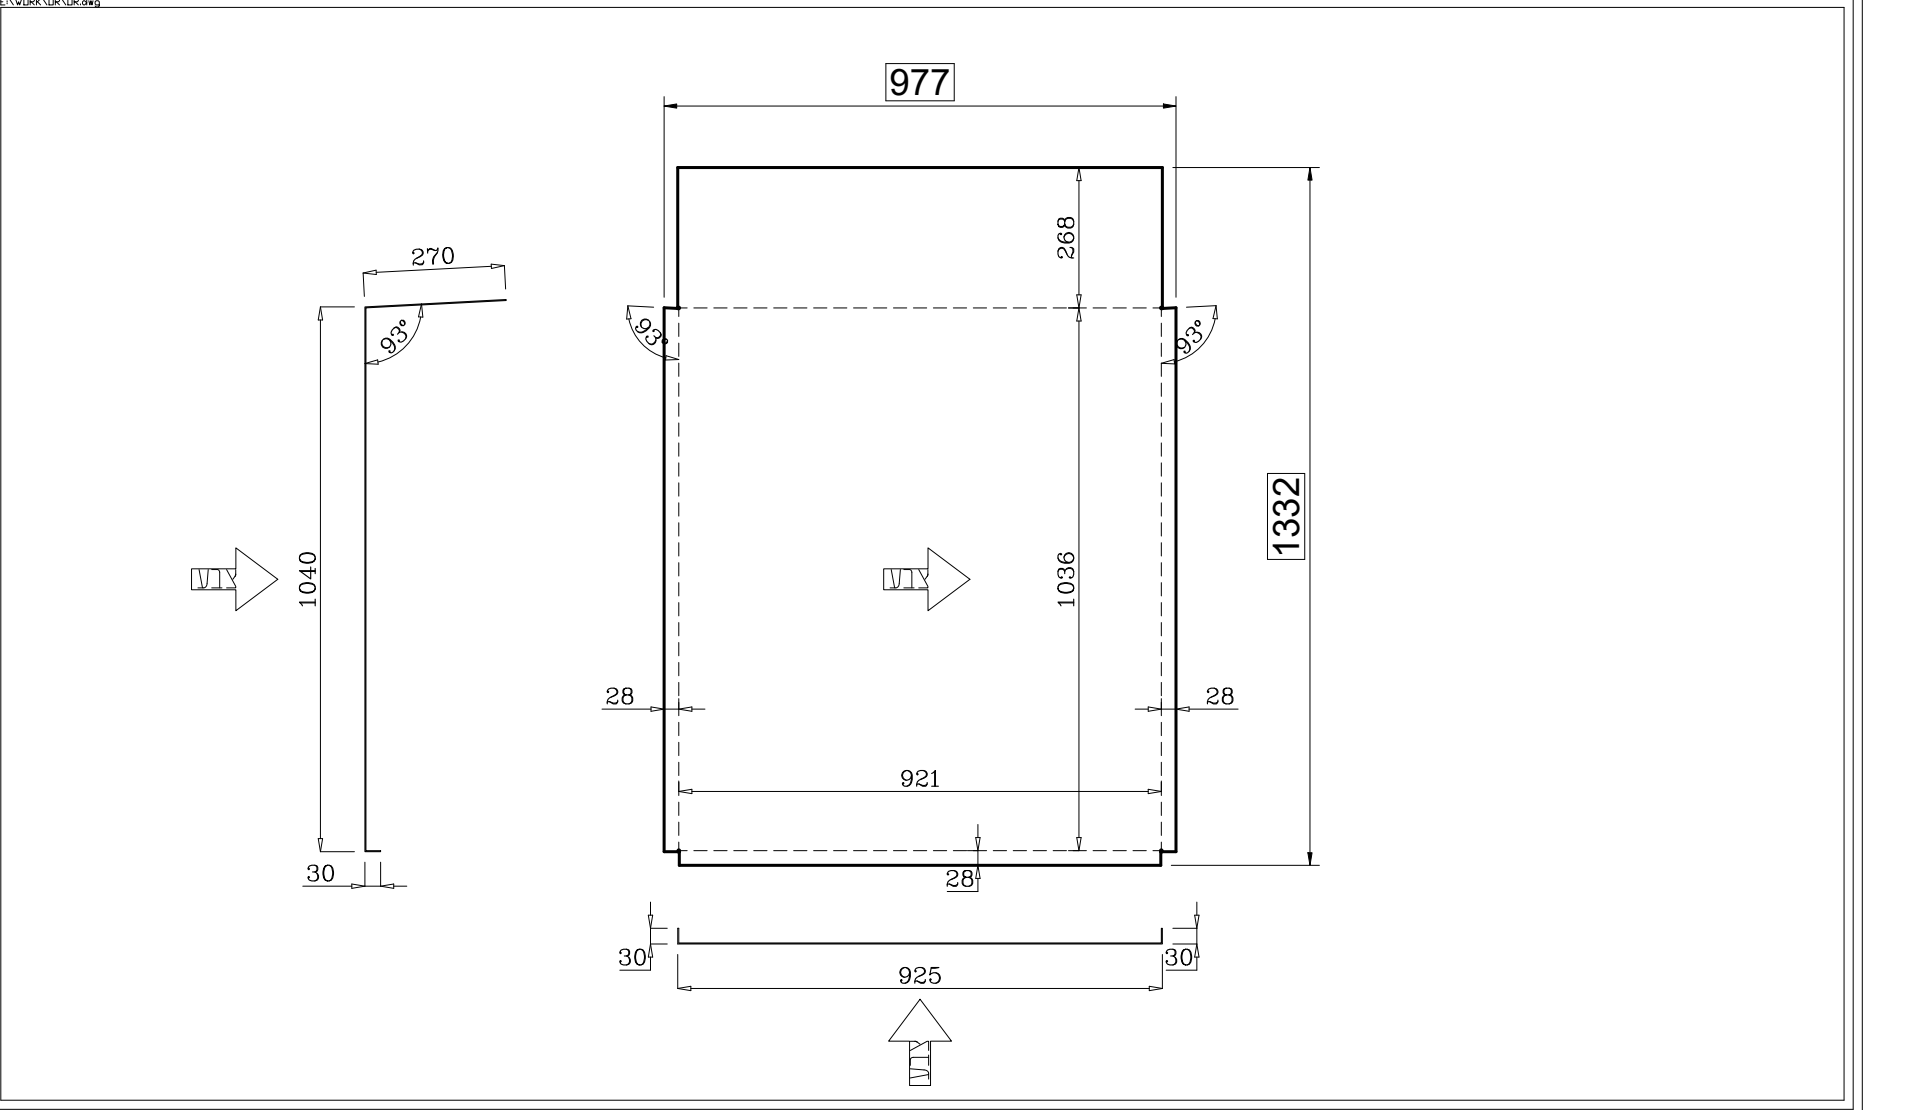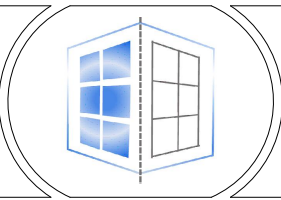

אלומיניום		סוג פח:	-	מתכנן: אור		שם הפרוייקט:		SH_05		מספר פנל:
RAL 9011 צבע		עובי פח:	2	תאריך: 12.03.2026		פרופסור שור 9 ת"א		רוחב	אורך	פריסת פח:
				הזמנה: SHOR_120326		מיקום הפנל בבנין:		1307	972	
						פלשונגים		1		מספר יחידות:

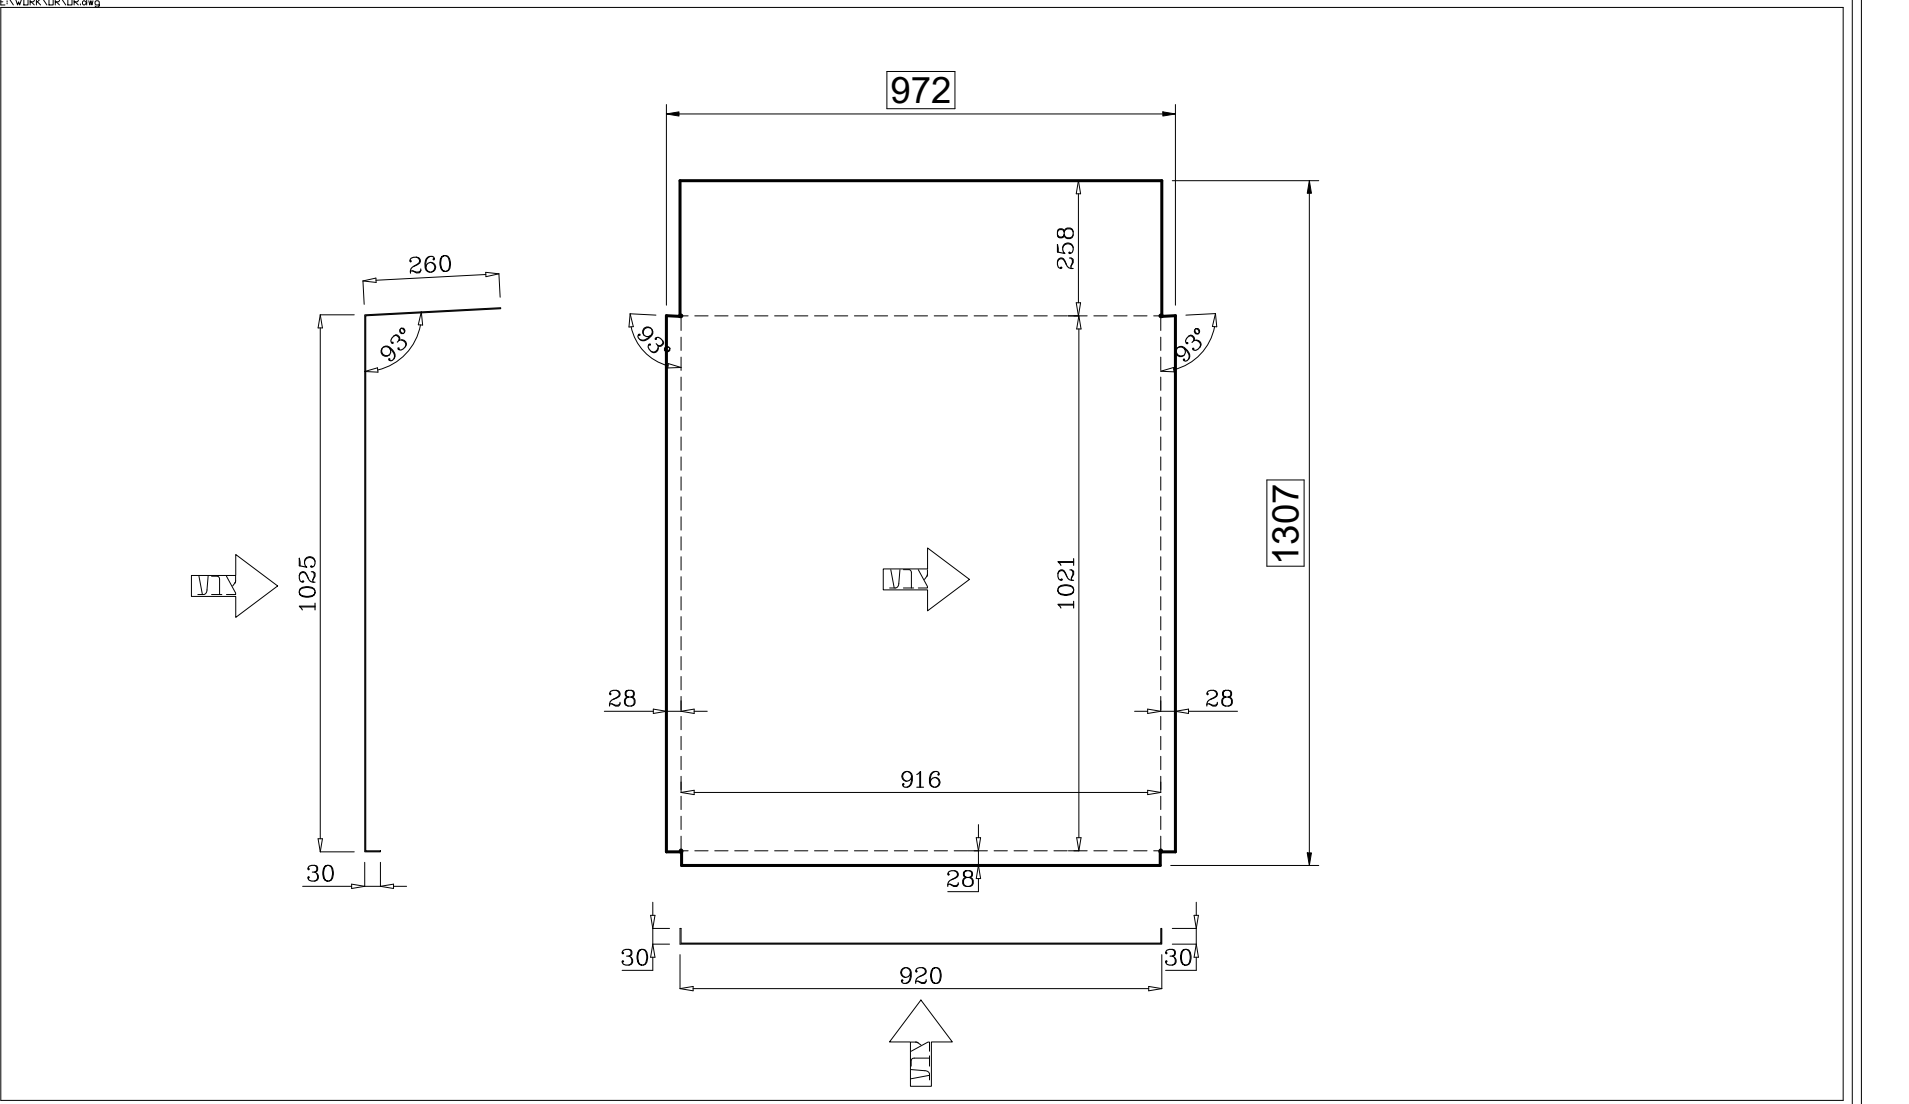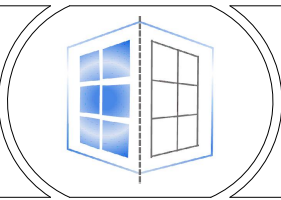

אלומיניום		סוג פח:	מתכנן: אור	שם הפרוייקט:		SH_07		מספר פנל:
RAL 9011		עובי פח:	תאריך: 12.03.2026	פרופסור שור 9 ת"א		רוחב	אורך	פריסת פח:
צבע		2	הזמנה:	מיקום הפנל בבניין:		523	2400	
			SHOR_120326	פלשונגים		5		מספר יחידות:

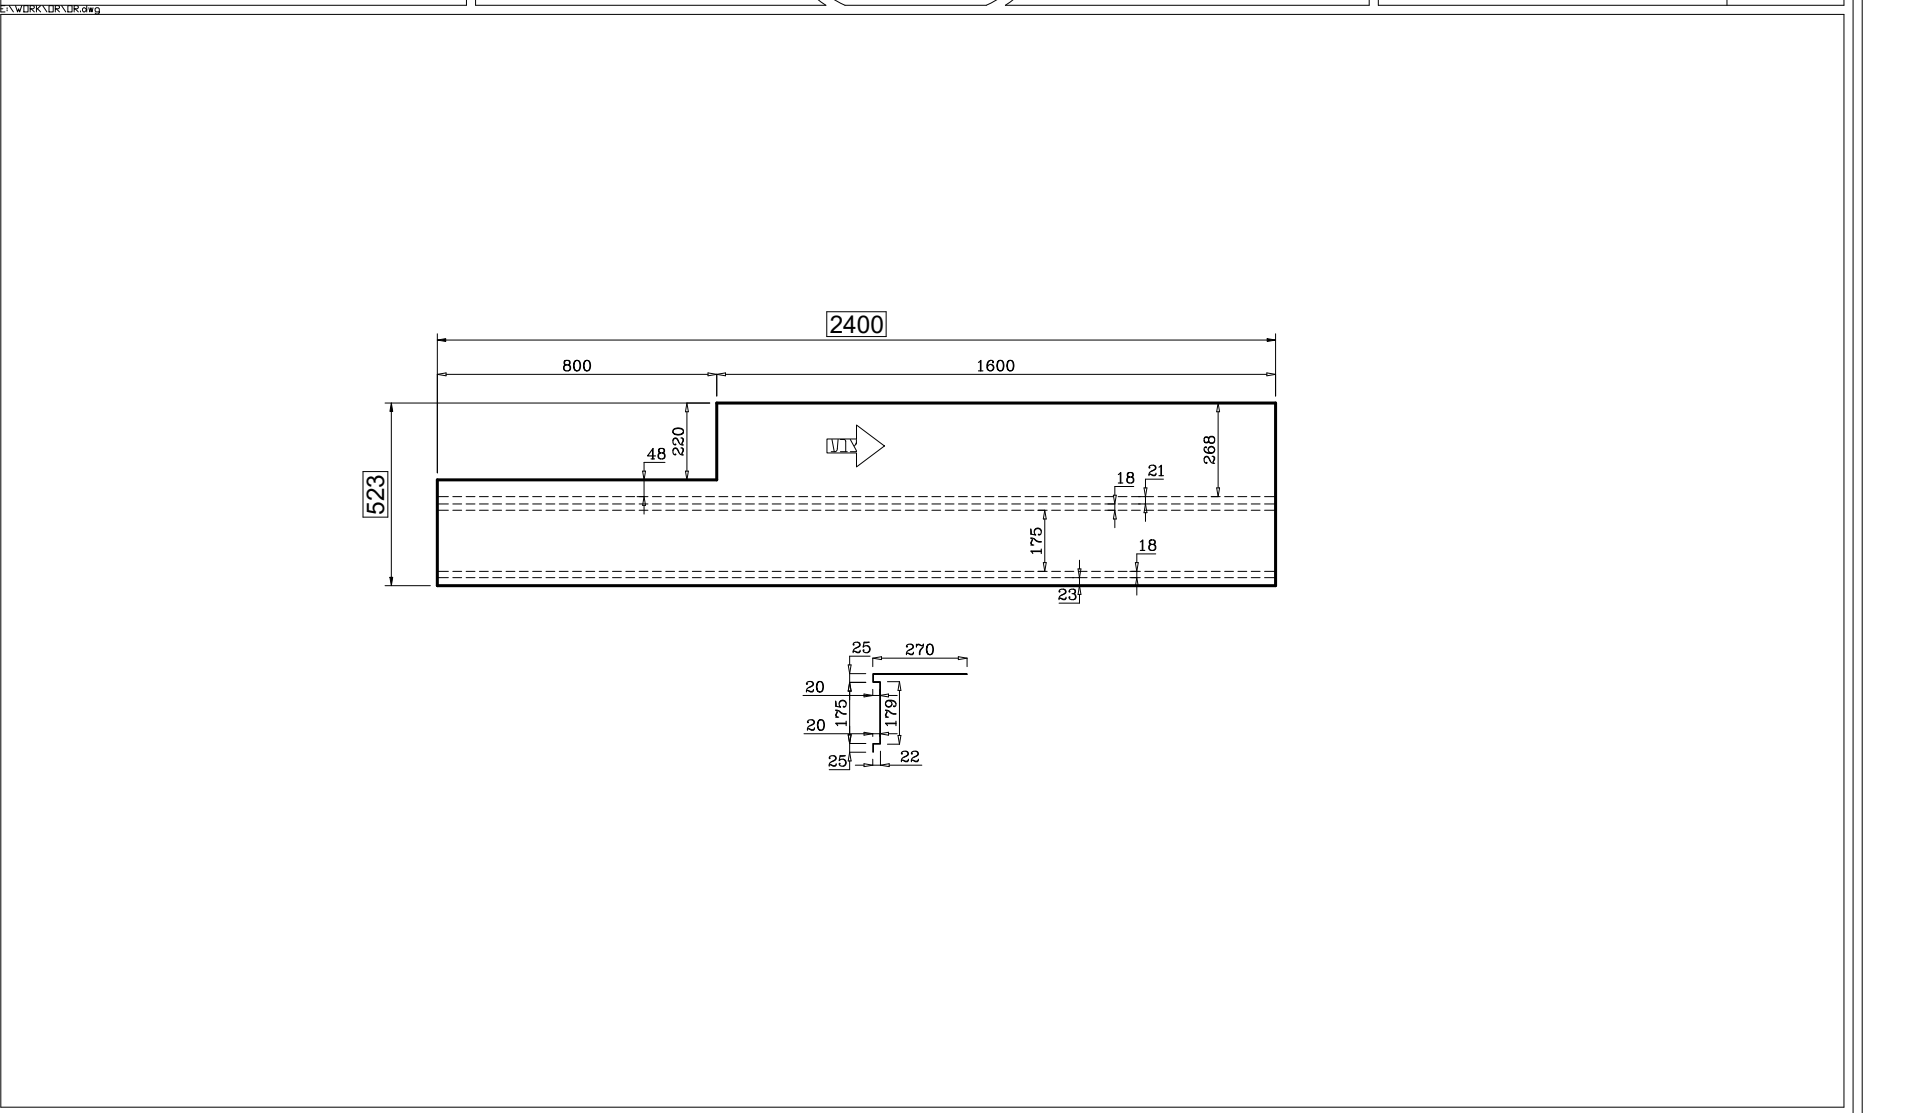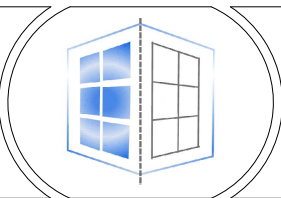


אלומיניום		סוג פח:	-	שם הפרוייקט:		SH_08		מספר פנל:
RAL 9011		צבע	2	מיקום הפנל בבנין:		רוחב	אורך	פריסת פח:
		עובי פח:		פלשונגים		523	2700	
						5		מספר יחידות:

מתכנן: אור

תאריך: 12.03.2026


הזמנה:

SHOR_120326


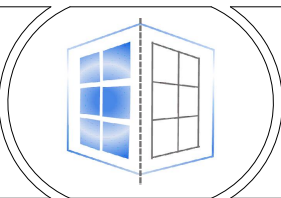


פרופסור שור 9 ת"א



מספר פנל:

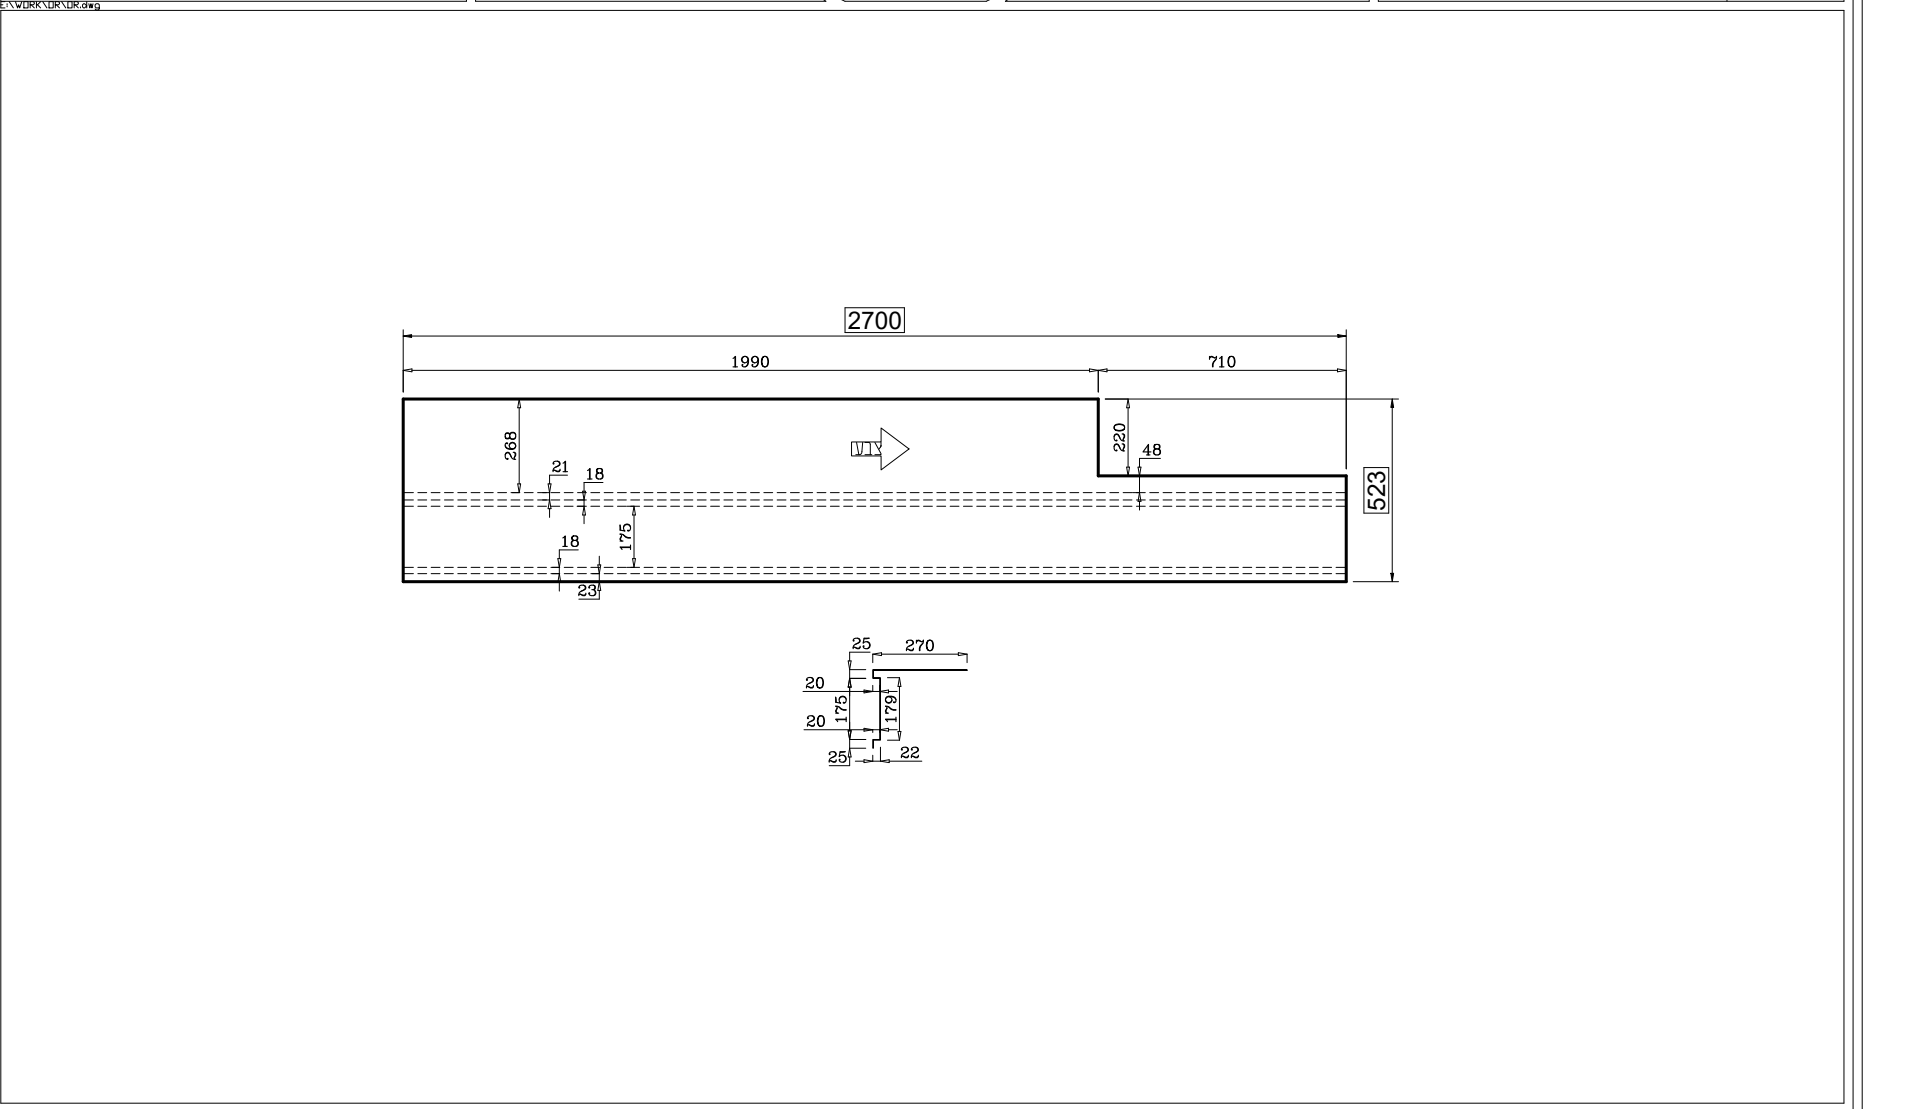


אלומיניום		סוג פח:	-	מתכנן: אור		שם הפרוייקט:		SH_15		מספר פנל:
RAL 9011 צבע		עובי פח:	2	תאריך: 12.03.2026		פרופסור שור 9 ת"א		רוחב		פריסת פח:
				הזמנה:		מיקום הפנל בבנין:		298		אורך
				SHOR_01		פלשווגים		1110		מספר יחידות:
								5		

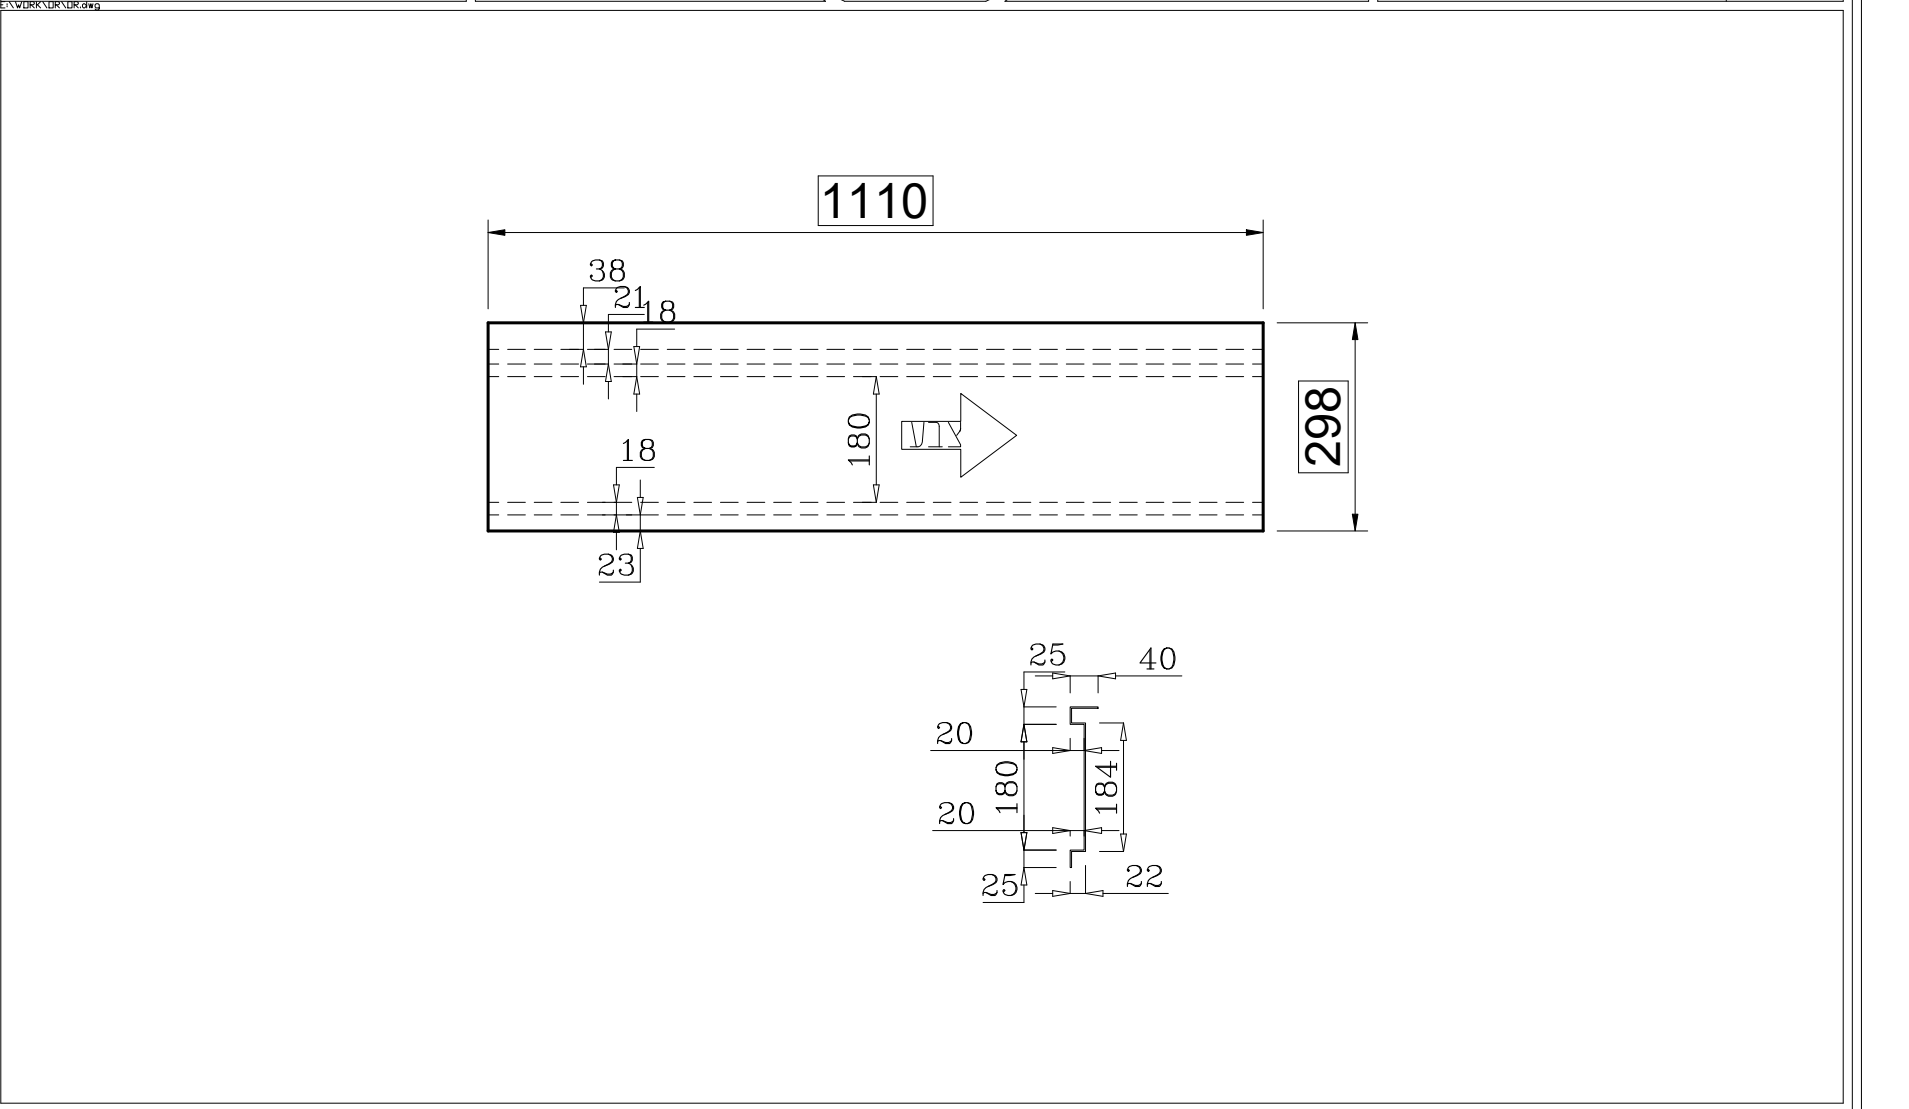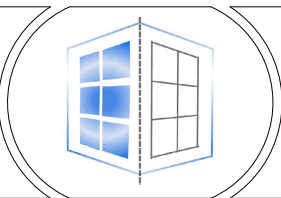


אלומיניום		סוג פח:	מתכנן: אור	שם הפרוייקט:	SH_17	מספר פנל:
RAL 9011		עובי פח:	תאריך: 12.03.2026	פרופסור שור 9 ת"א	רוחב: 1312	פריסת פח:
צבע: 2			הזמנה: SHOR_120326	מיקום הפנל בבנין:	אורך: 972	
				פלשווגים	3	מספר יחידות:

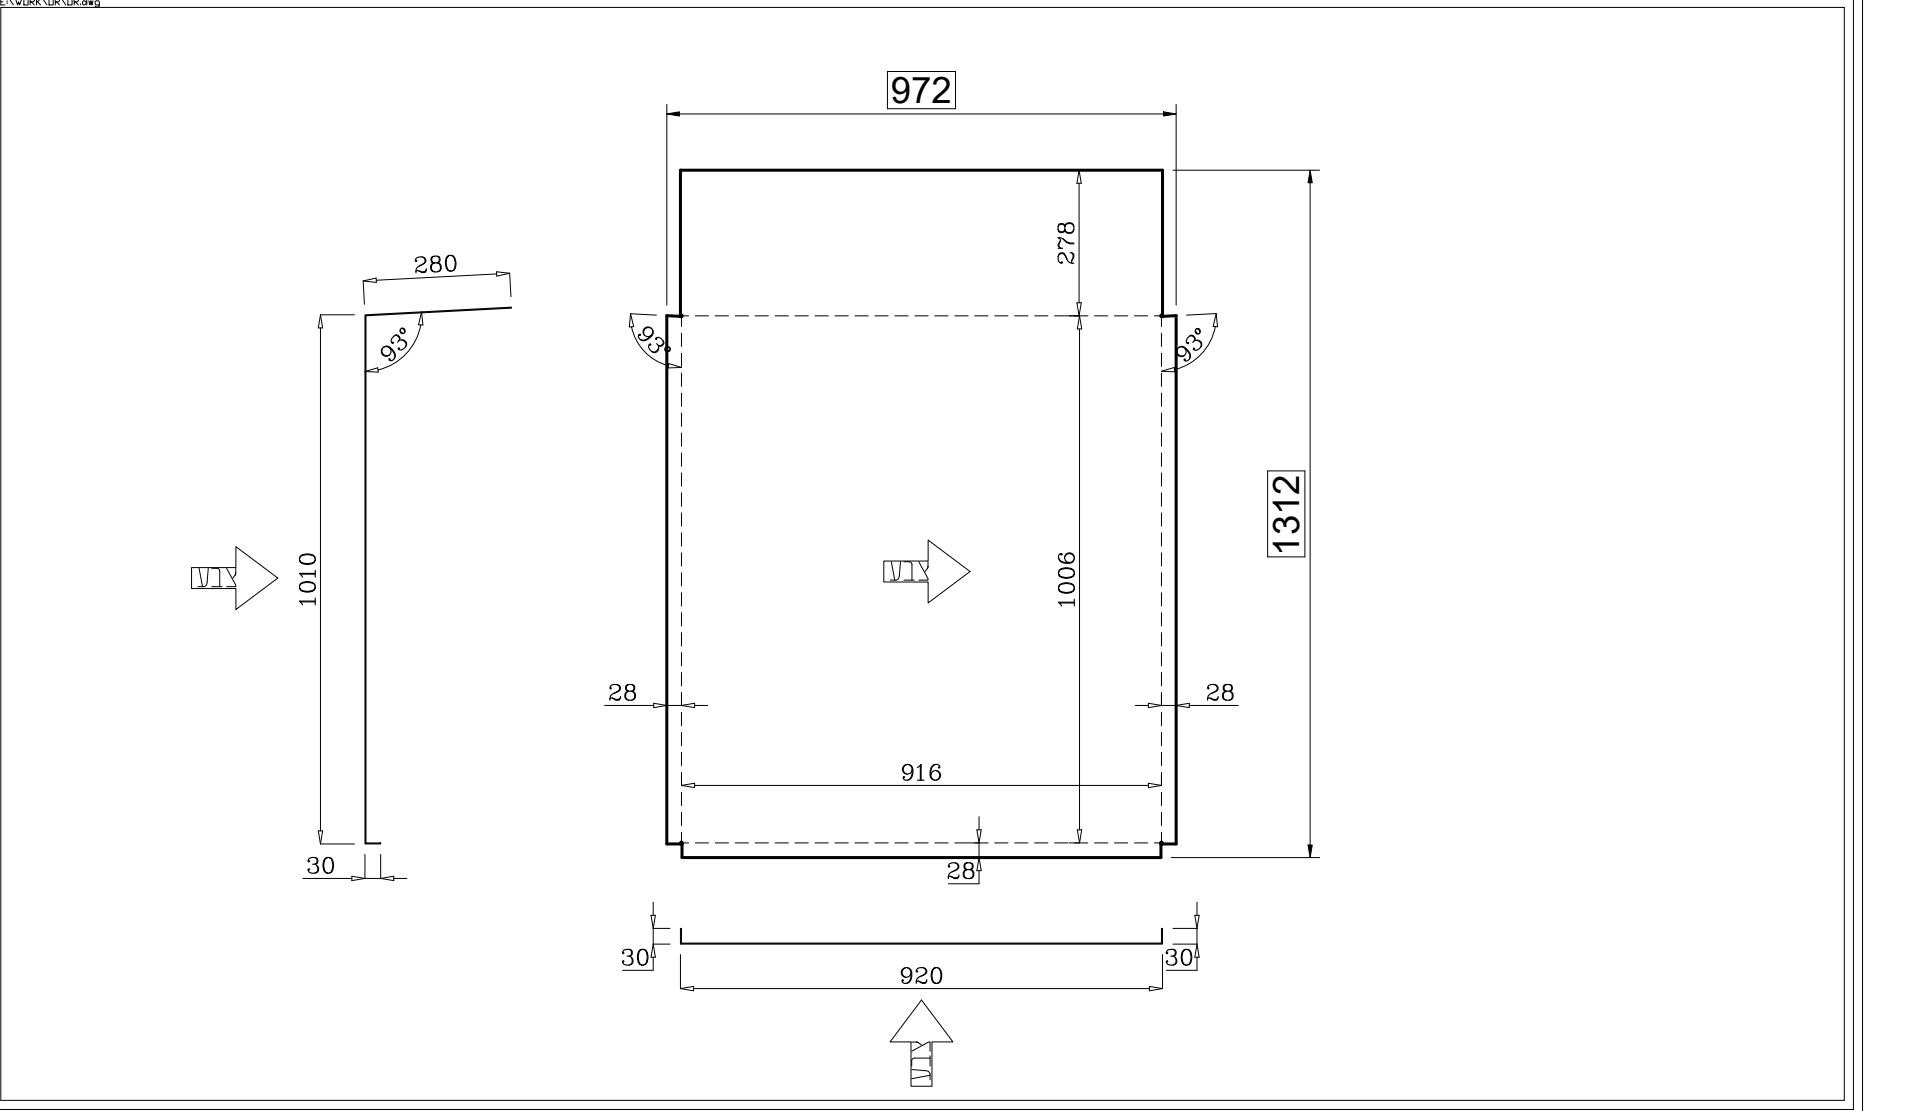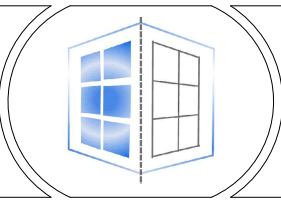



אלומיניום	-	סוג פח:	מתכנן: אור	שם הפרוייקט:	SH_26	מספר פנל:
RAL 9011	2	עובי פח:	תאריך: 12.03.2026	פרופסור שור 9 ת"א	רוחב 313	פריסת פח:
			הזמנה: SHOR_01	מיקום הפנל בבנין:	אורך 3500	מספר יחידות:
				פלשונגים	3	

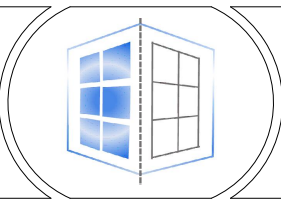


C:\WORK\UR\UR.dwg

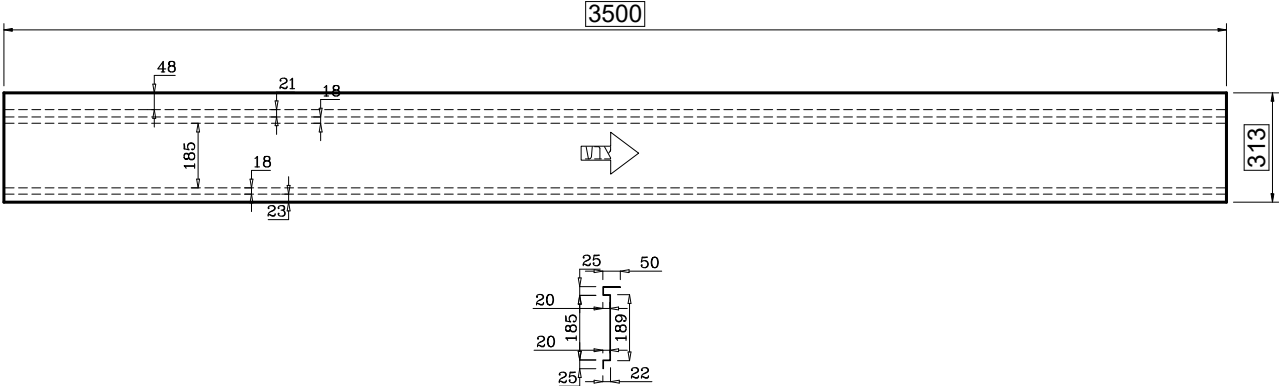



אלומיניום		סוג פח:	מתכנן: אור	שם הפרוייקט:	SH_42		מספר פנל:
RAL 9011	צבע	2	תאריך: 12.03.2026	פרופסור שור 9 ת"א	רוחב	אורך	פריסת פח:
		עובי פח:	הזמנה:	מיקום הפנל בבניין:	1322	1642	מספר יחידות:
			SHOR_120326	פלשונגים	1		

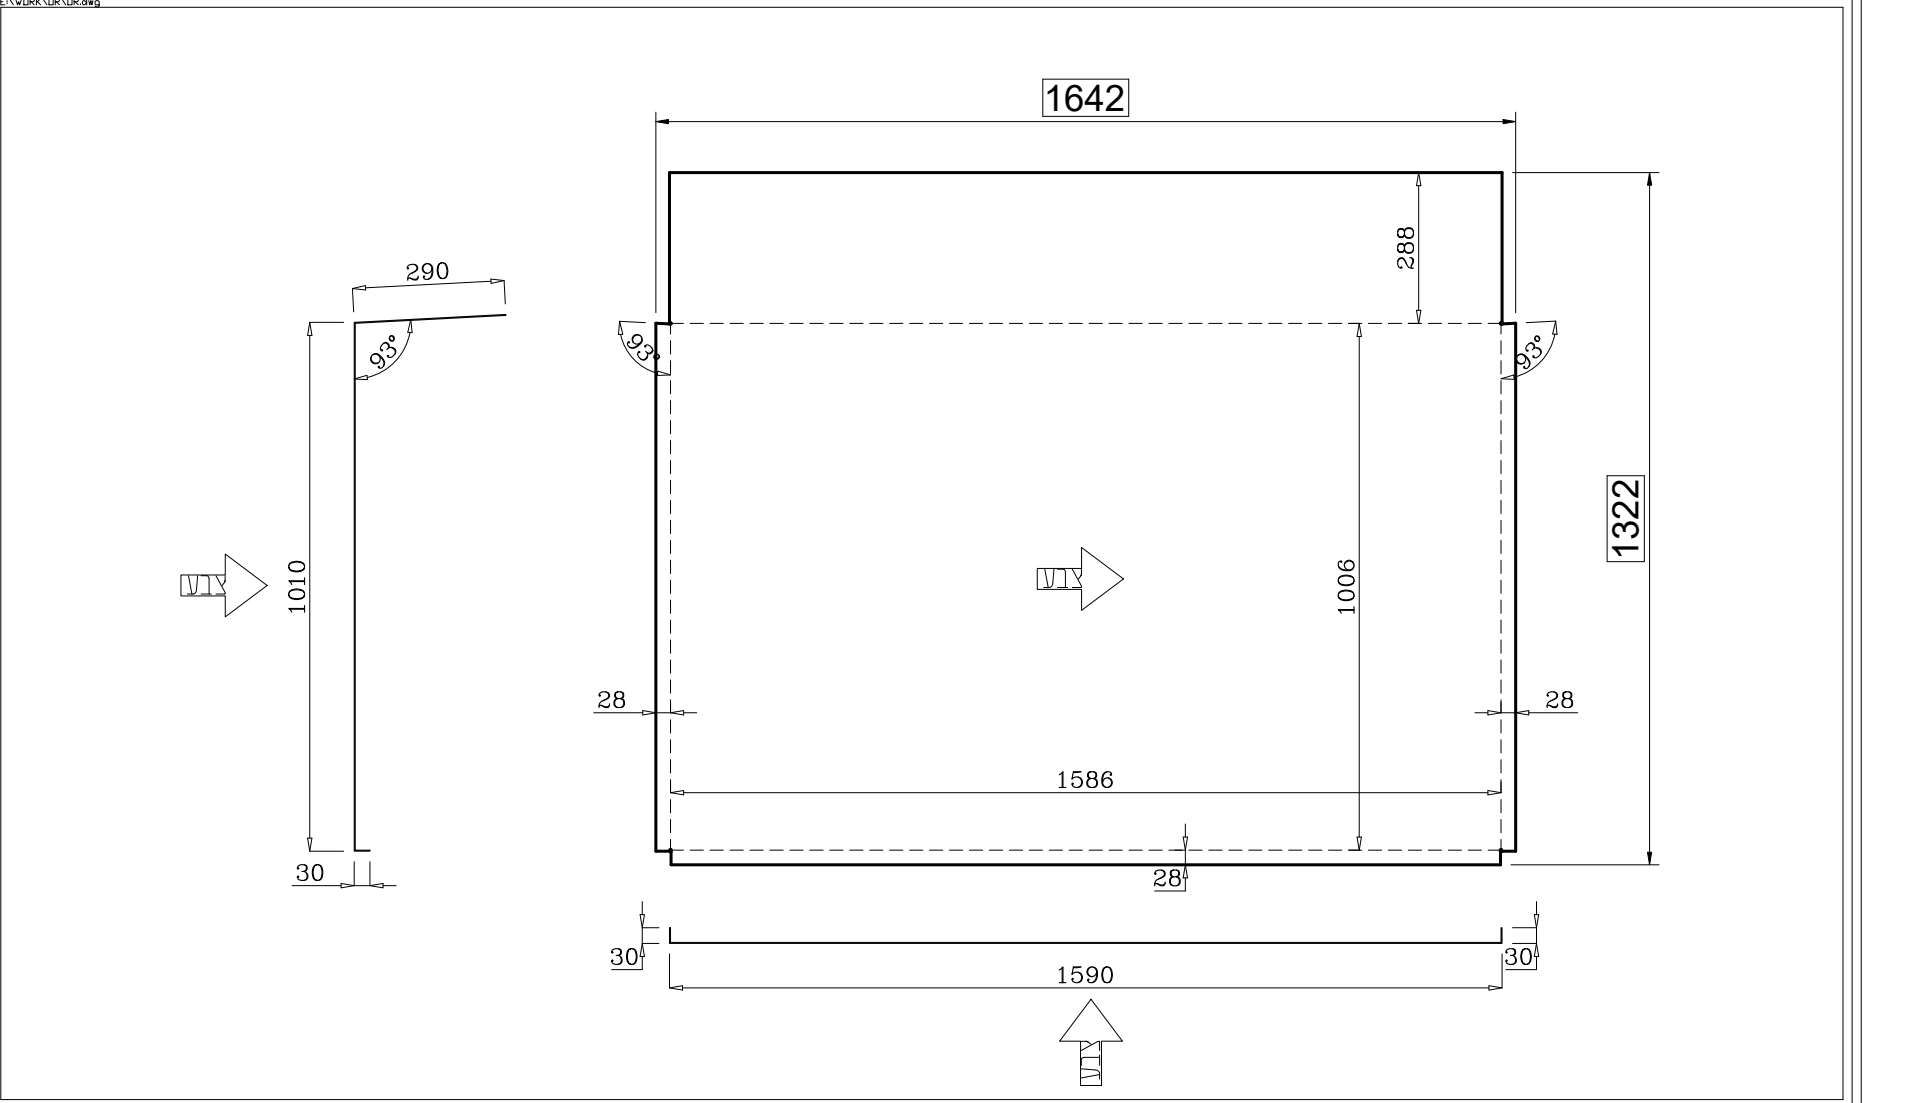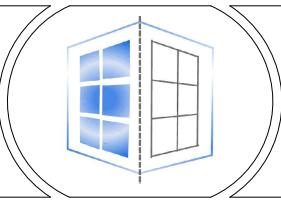



אלומיניום		סוג פח:	-	מתכנן: אור		שם הפרוייקט:		SH_44A		מספר פנל:
RAL 9011		עובי פח:	2	תאריך: 12.03.2026		פרופסור שור 9 ת"א		רוחב	אורך	פריסת פח:
צבע				הזמנה: SHOR_01		מיקום הפנל בבניין:		523	1600	
						פלשונגים		1		מספר יחידות:

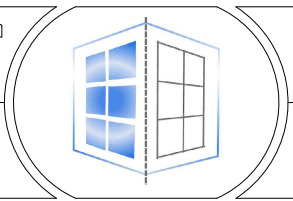

\\WORK\UR\UR.dwg

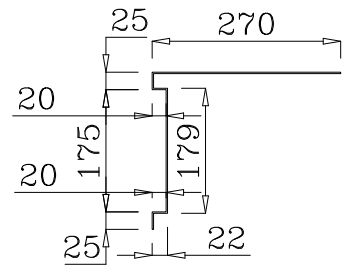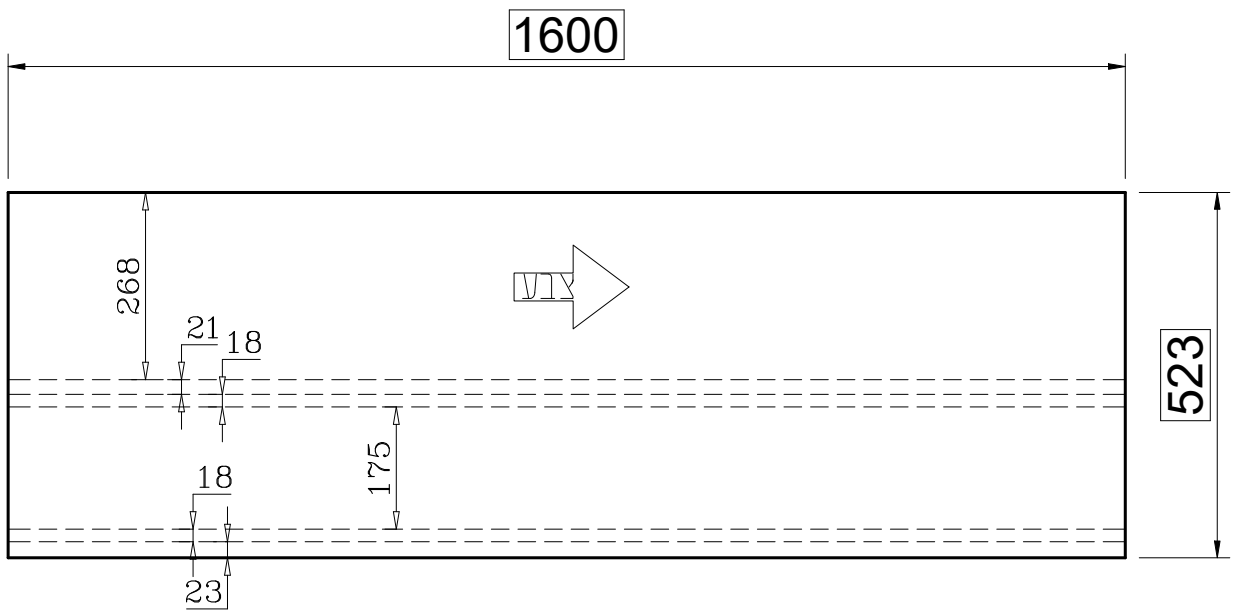

אלומיניום		סוג פח:	-	מתכנן: אור		שם הפרוייקט:		SH_44B		מספר פנל:
RAL 9011		צבע:	2	תאריך: 12.03.2026		פרופסור שור 9 ת"א		רוחב	אורך	פריסת פח:
		עובי פח:		הזמנה:		מיקום הפנל בבנין:		303	3450	
				SHOR_01		פלשונגים		1		מספר יחידות:

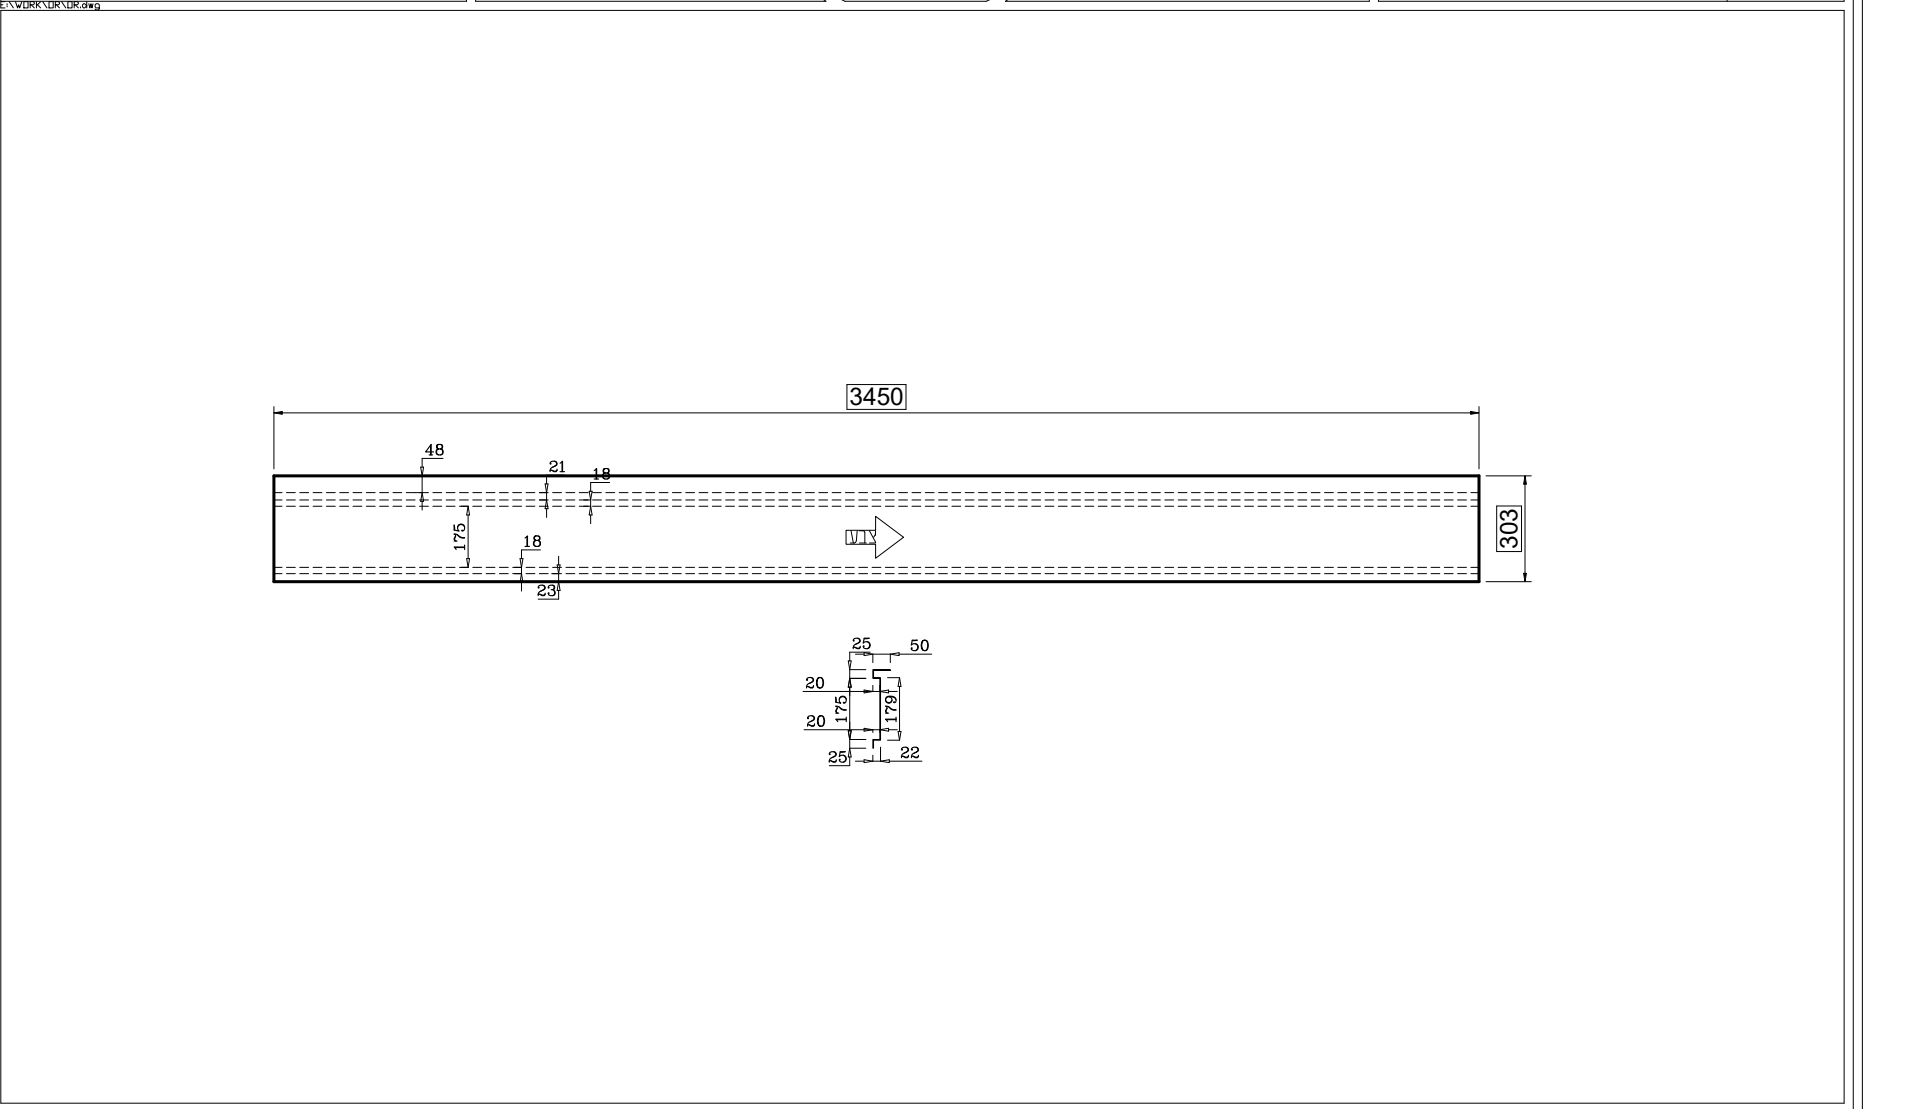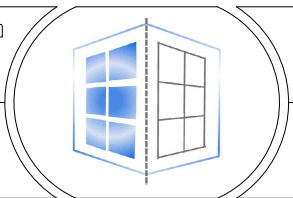

אלומיניום	סוג פח:	מתכנן: אור	שם הפרוייקט:	SH_44C	מספר פנל:
RAL 9011	עובי פח:	תאריך: 12.03.2026	פרופסור שור 9 ת"א	רוחב: 1317	פריסת פח:
צבע	2	הזמנה: SHOR_120326	מיקום הפנל בבנין:	אורך: 972	מספר יחידות:
			פלשונגים	1	

